



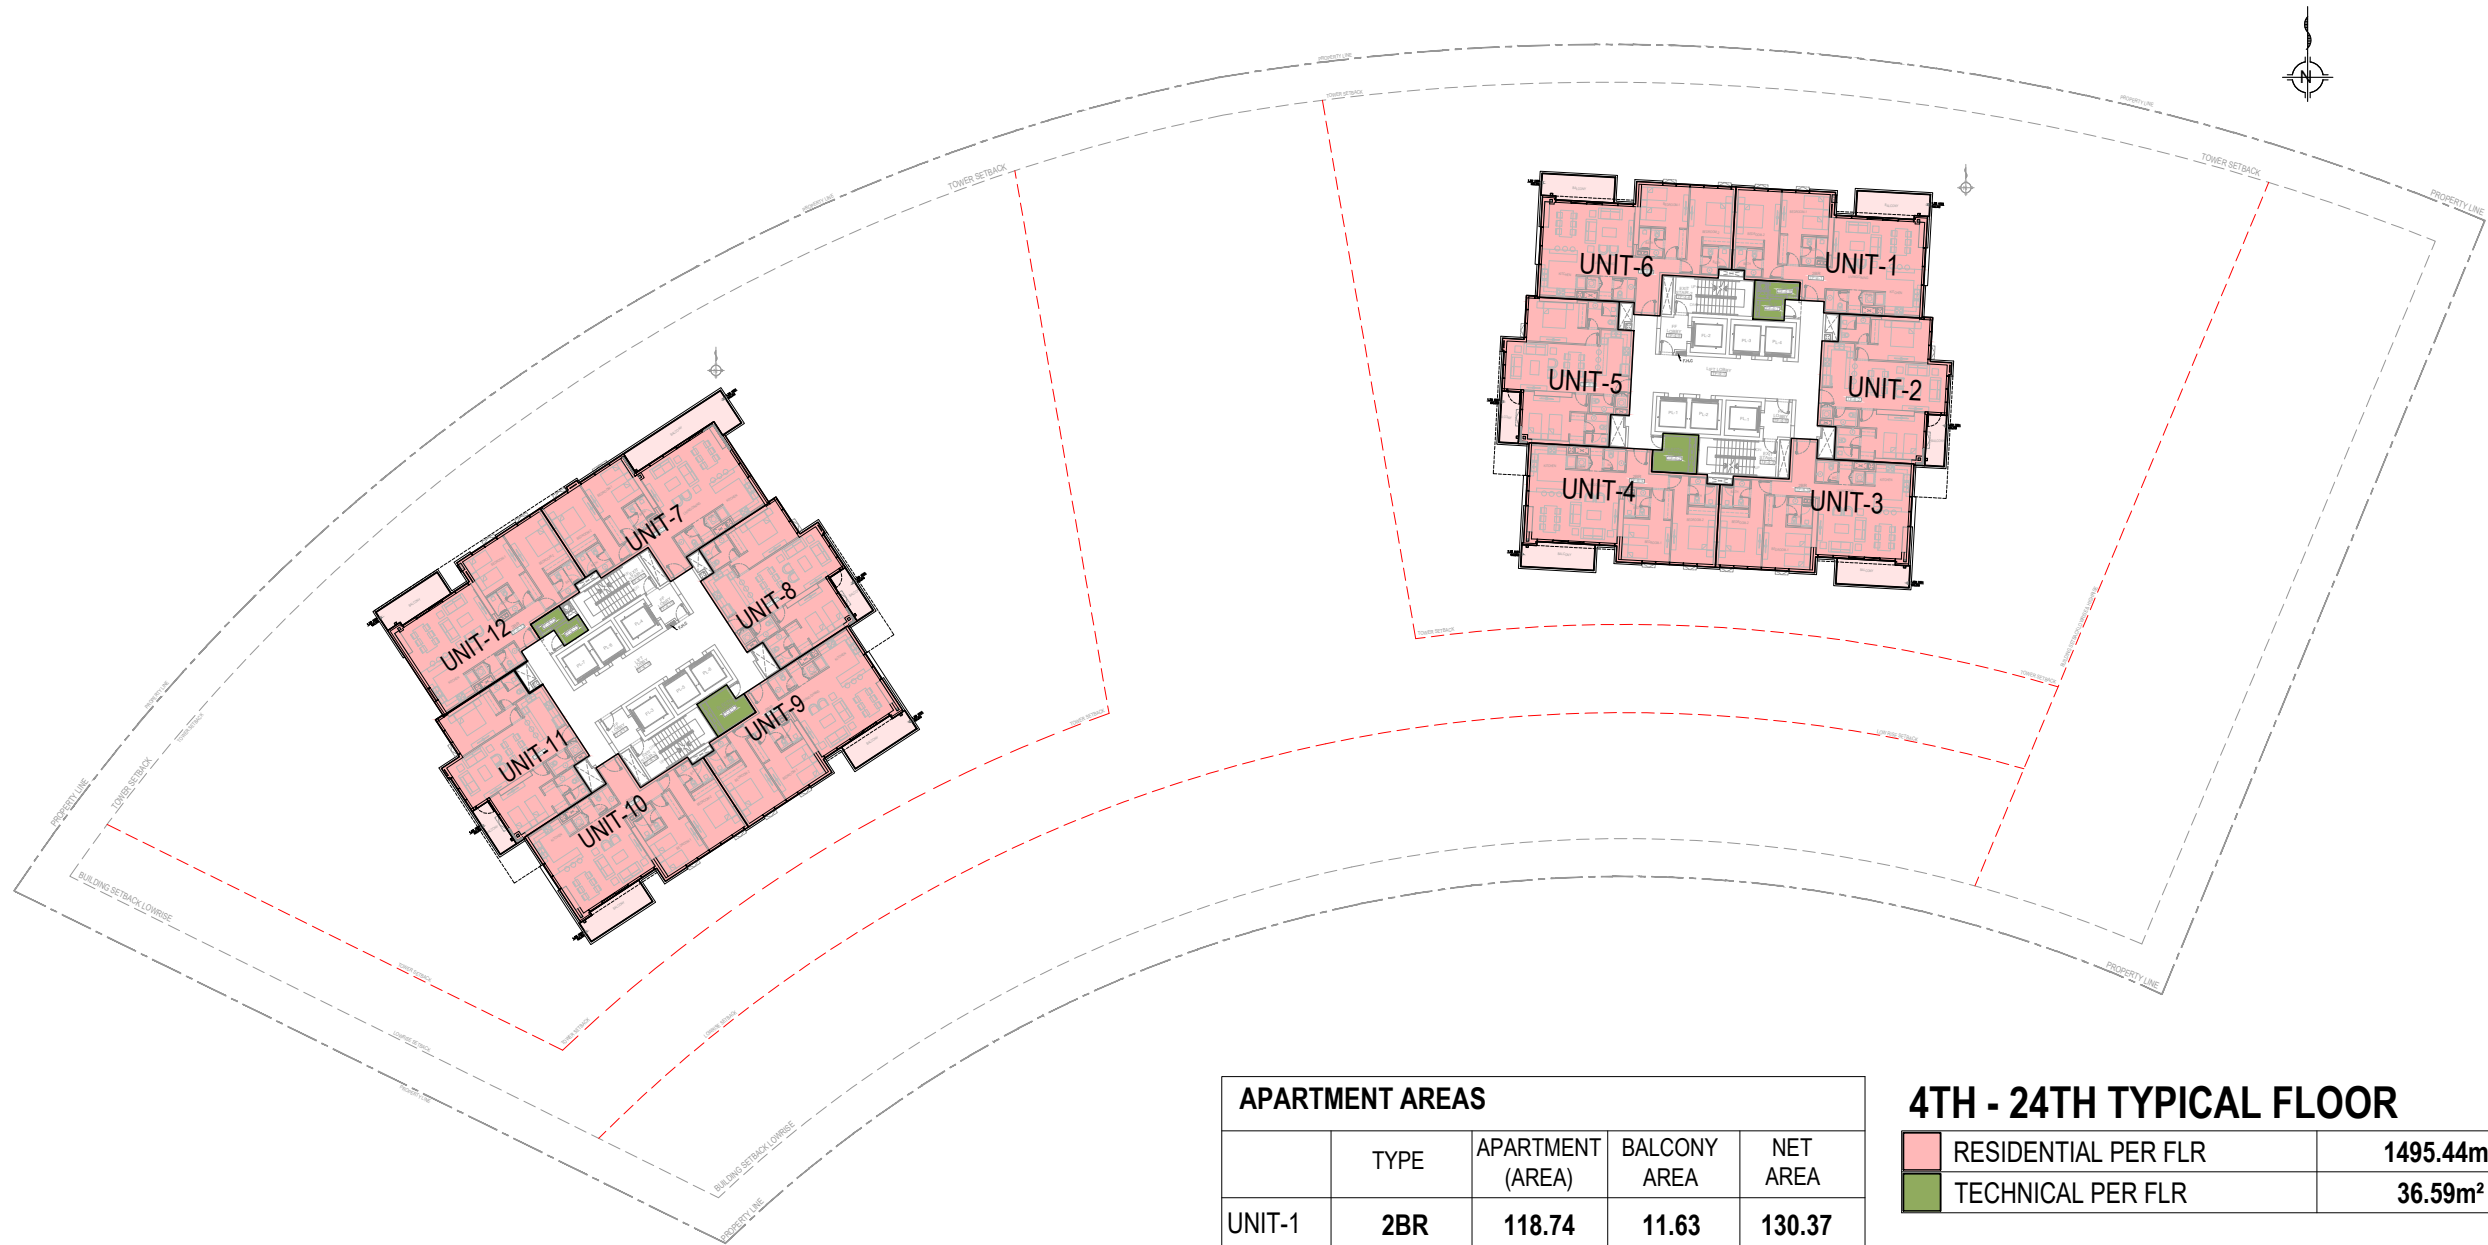

APARTMENT AREAS				
	TYPE	APARTMENT (AREA)	BALCONY AREA	NET AREA
UNIT-1	2BR	118.74	11.63	130.37
UNIT-2	2BR	100.60	6.32	106.92
UNIT-3	2BR	122.36	11.63	133.99
UNIT-4	2BR	119.23	11.63	130.86
UNIT-5	2BR	100.60	6.32	106.92
UNIT-6	2BR	122.53	11.63	134.16
UNIT-7	2BR	123.44	18.90	142.34
UNIT-8	2BR	100.58	6.32	106.90
UNIT-9	2BR	119.21	11.58	130.79
UNIT-10	2BR	122.33	11.63	133.96
UNIT-11	2BR	100.61	6.32	106.93
UNIT-12	2BR	119.67	11.63	131.30
TOTAL		1369.90	125.54	1495.44


4TH - 24TH TYPICAL FLOOR		
RESIDENTIAL PER FLR		1495.44m²
TECHNICAL PER FLR		36.59m²
RESIDENTIAL - 21 FLOORS		31404.24m²
TECHNICAL - 21 FLOORS		768.35m²

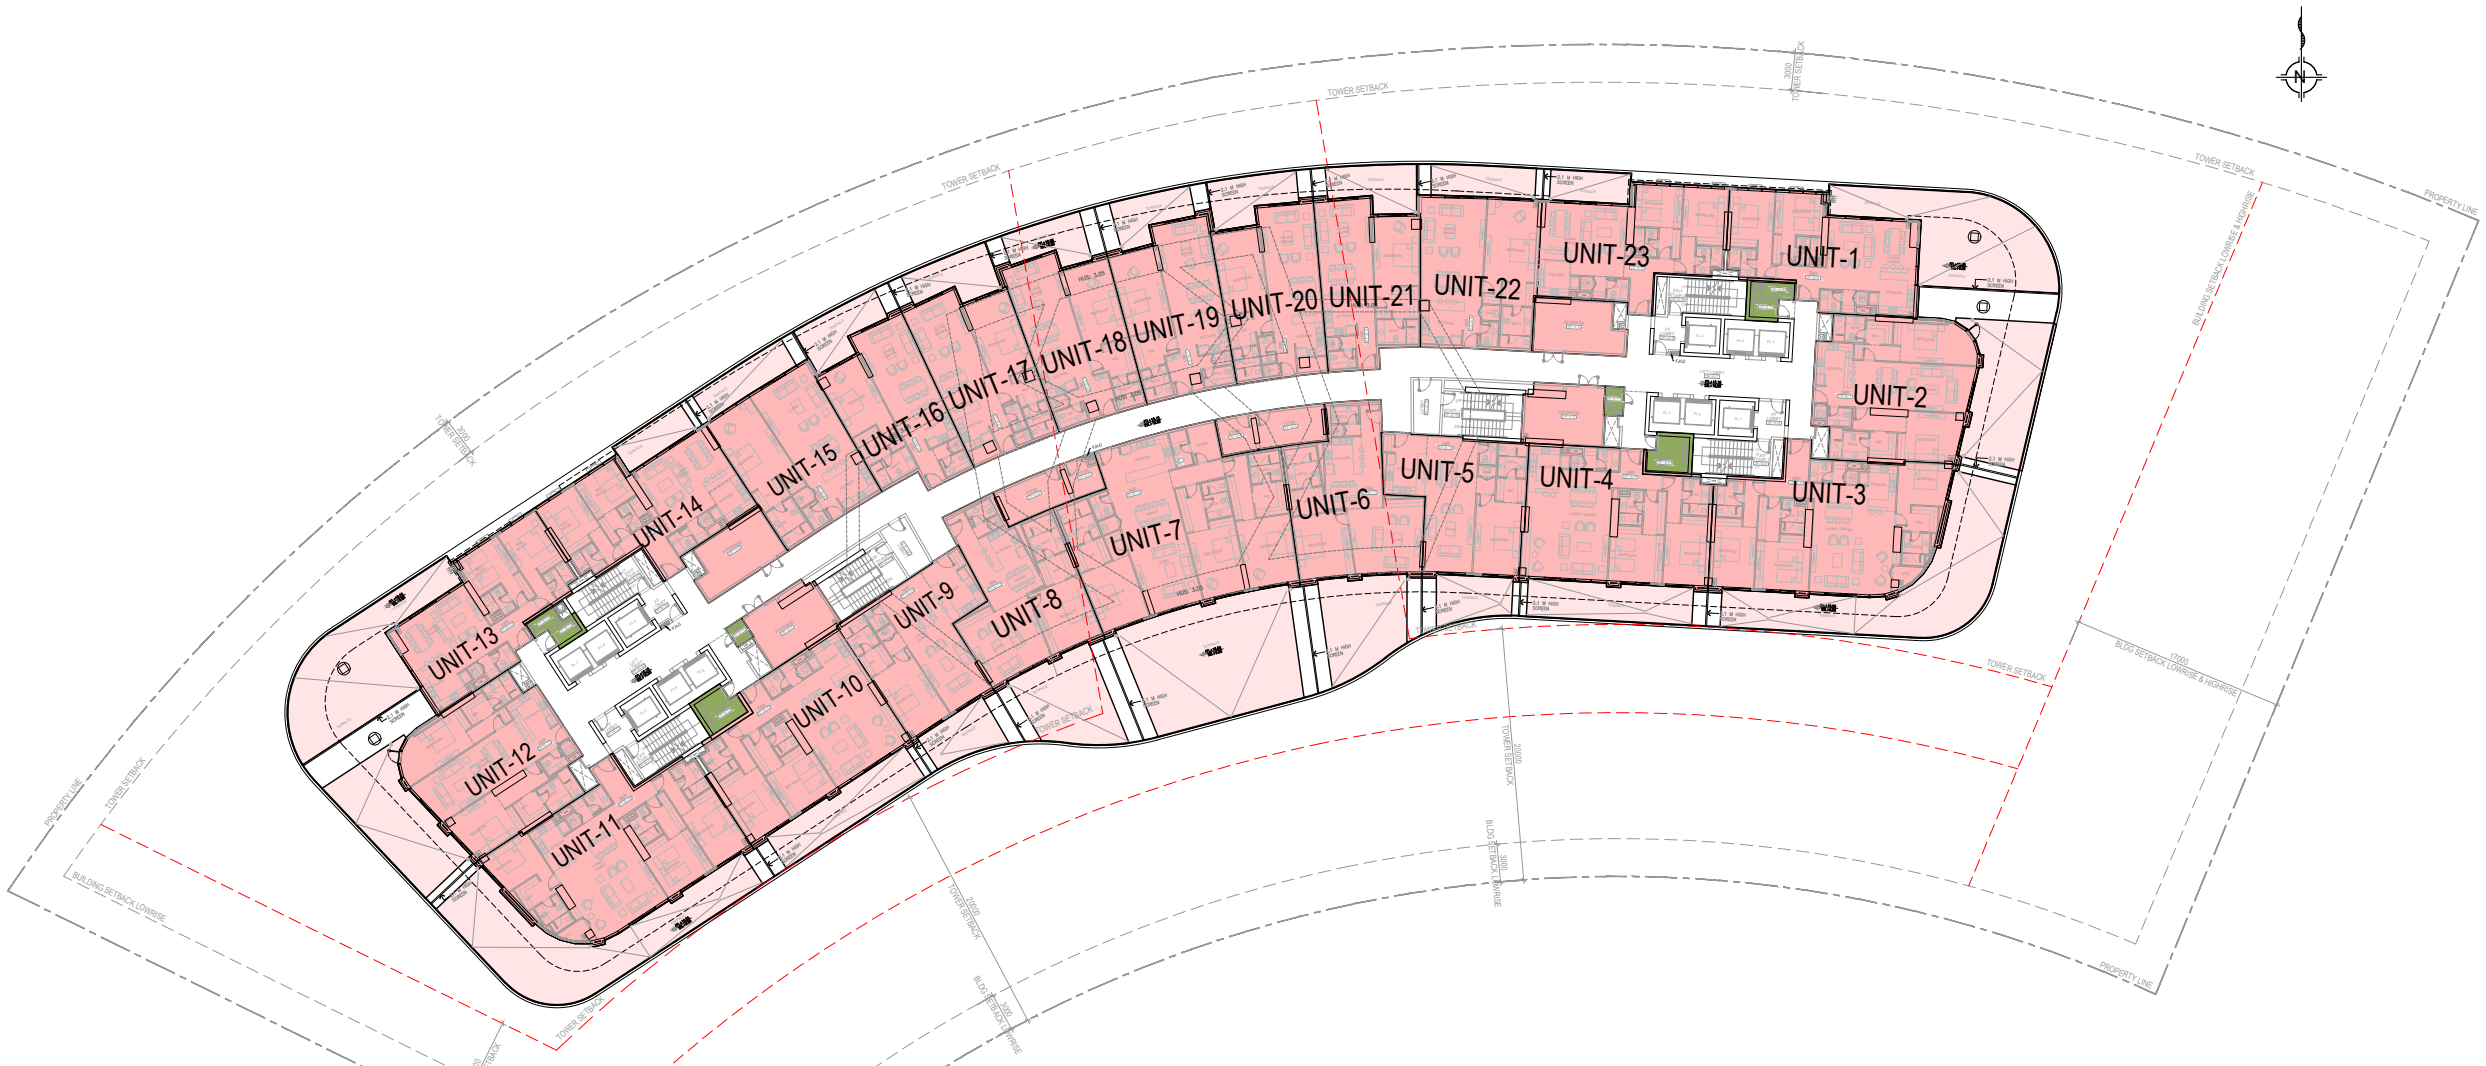

APARTMENT AREAS				
	TYPE	APARTMENT (AREA)	BALCONY AREA	NET AREA
UNIT-1	2BR	118.39	91.35	209.74
UNIT-2	2BR	137.44	63.10	200.54
UNIT-3	3BR	187.10	111.17	298.27
UNIT-4	2BR	150.43	39.19	189.62
UNIT-5	1BR	104.04	21.02	125.06
UNIT-6	1BR	114.76	48.09	162.85
UNIT-7	3BR	220.28	121.51	341.79
UNIT-8	1BR	114.89	48.02	162.91
UNIT-9	1BR	103.46	21.00	124.46
UNIT-10	2BR	153.43	39.17	192.60
UNIT-11	3BR	185.88	110.68	296.56
UNIT-12	2BR	137.14	60.37	197.51

APARTMENT AREAS				
	TYPE	APARTMENT (AREA)	BALCONY AREA	NET AREA
UNIT-13	2BR	118.47	91.10	209.57
UNIT-14	2BR	119.59	15.59	135.18
UNIT-15	1BR	111.30	20.21	131.51
UNIT-16	1BR	98.15	22.71	120.86
UNIT-17	1BR	103.68	22.34	126.02
UNIT-18	1BR	104.76	19.59	124.35
UNIT-19	1BR	104.79	19.58	124.37
UNIT-20	1BR	103.66	22.34	126.00
UNIT-21	1BR	98.13	22.69	120.82
UNIT-22	1BR	112.46	20.79	133.25
UNIT-23	2BR	117.55	15.57	133.12
TOTAL		2919.78	1067.18	3986.96

SECOND FLOOR LEVEL		
RESIDENTIAL		4159.48m²
TECHNICAL		49.84m²

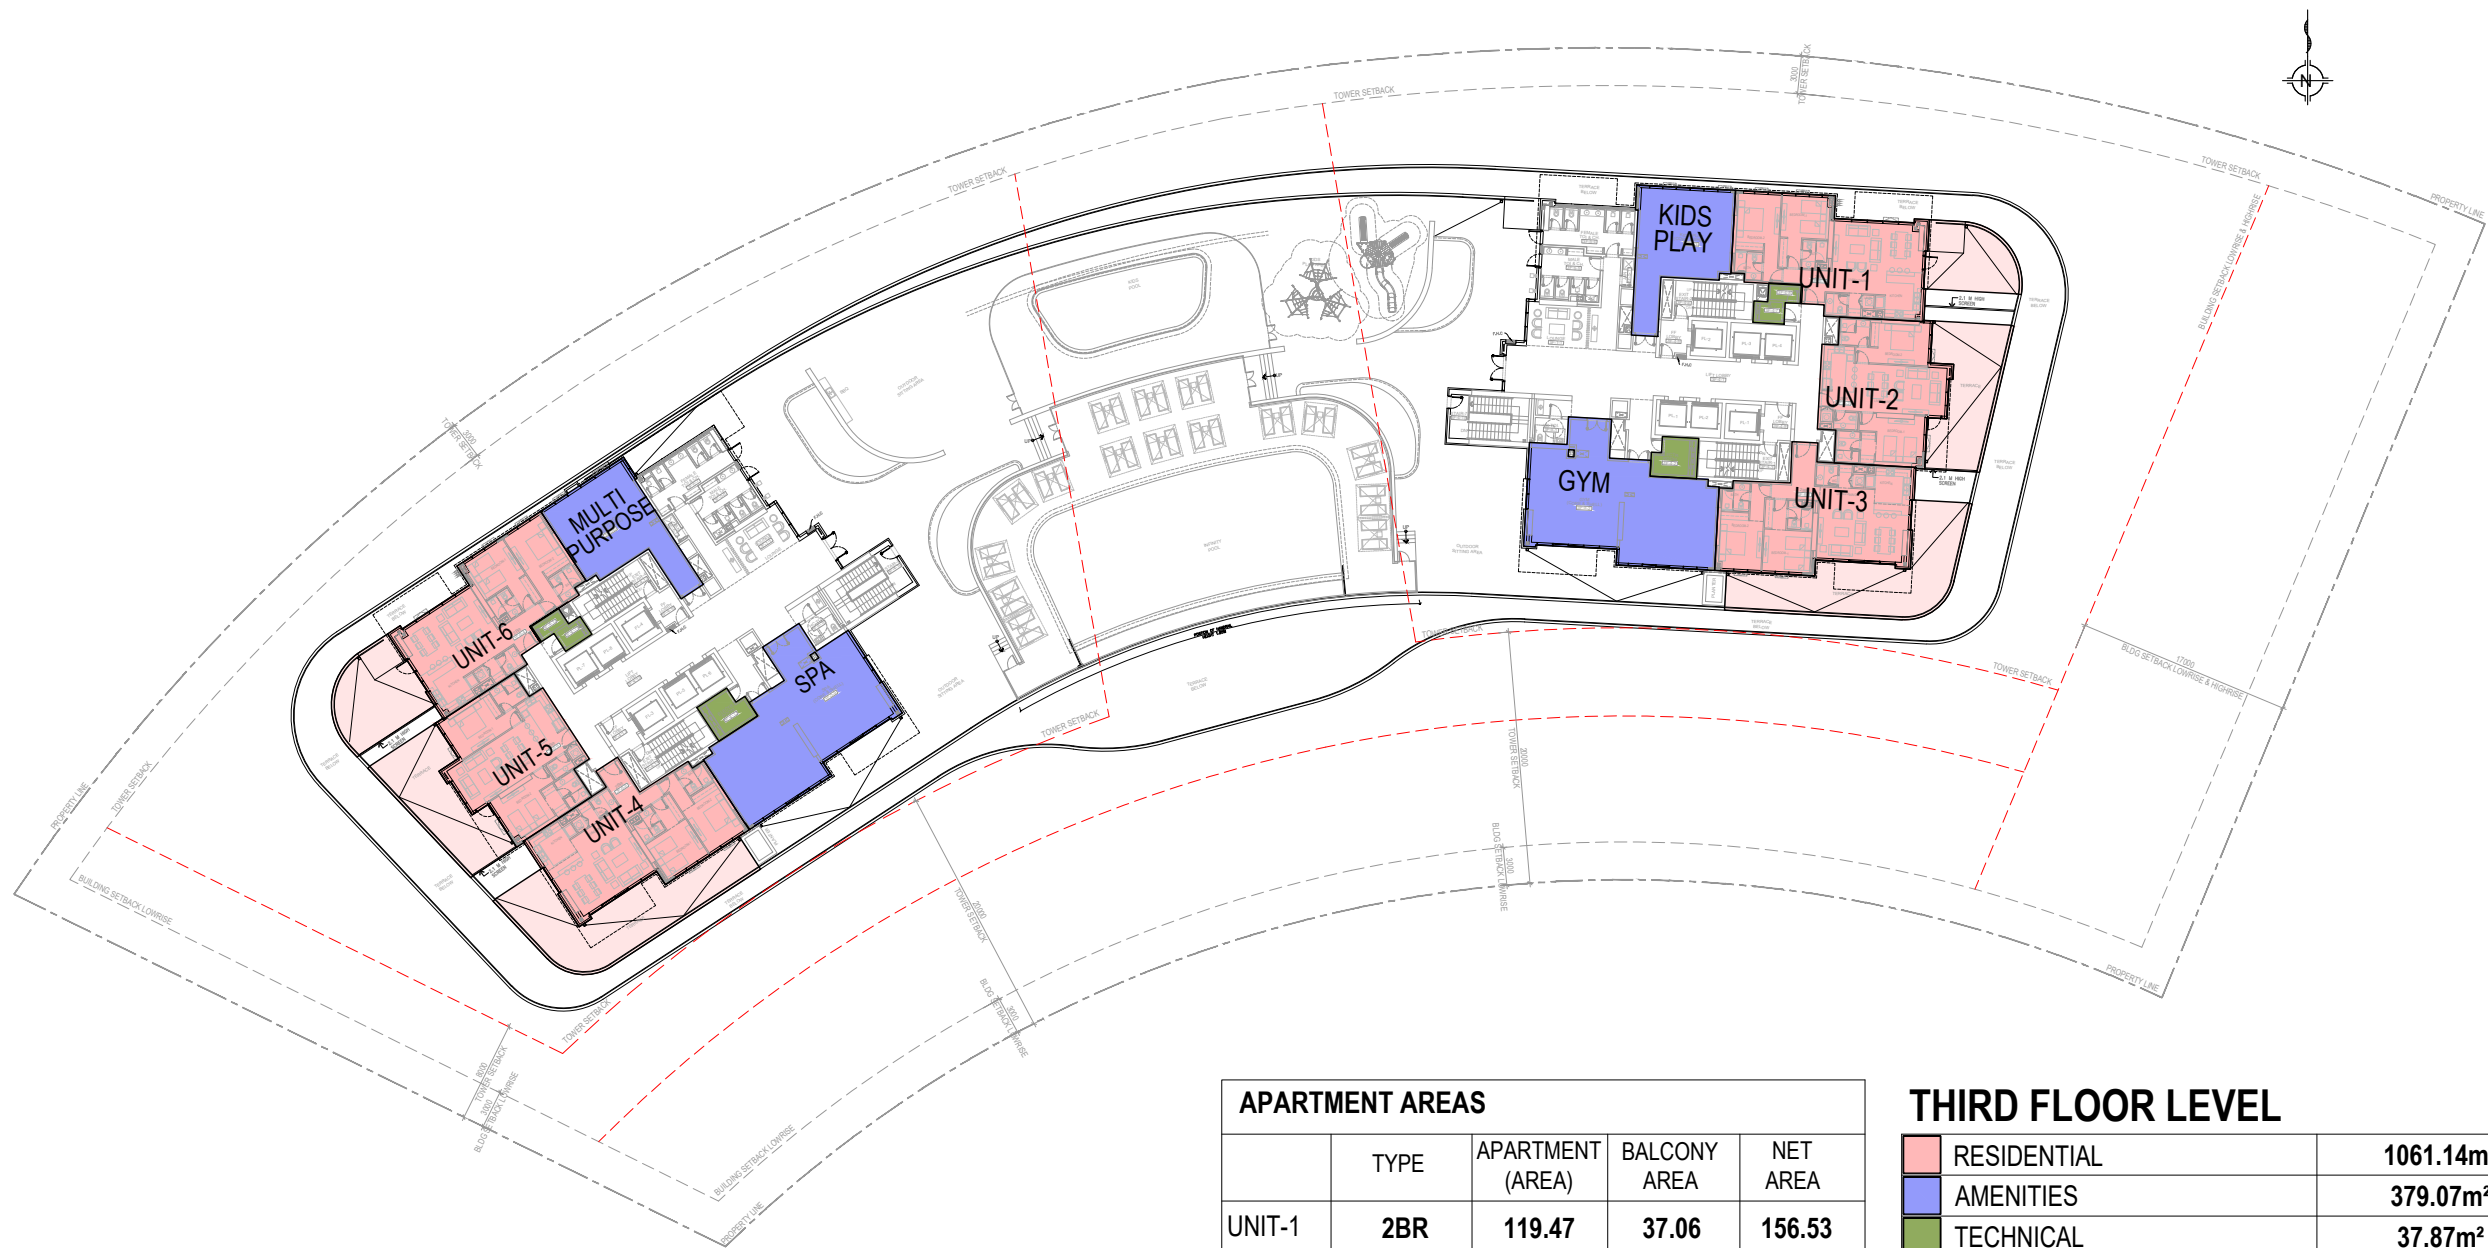

APARTMENT AREAS				
	TYPE	APARTMENT (AREA)	BALCONY AREA	NET AREA
UNIT-1	2BR	119.47	37.06	156.53
UNIT-2	2BR	101.02	56.75	157.77
UNIT-3	2BR	123.07	88.32	211.39
UNIT-4	2BR	123.07	88.32	211.39
UNIT-5	2BR	101.02	56.75	157.77
UNIT-6	2BR	119.47	46.82	166.29
TOTAL		687.12	374.02	1061.14

THIRD FLOOR LEVEL		
RESIDENTIAL		1061.14m²
AMENITIES		379.07m²
TECHNICAL		37.87m²

AMENITIES - AREAS	
1. KIDS PLAY	64.79
2. GYM	125.32
3. SPA	124.17
4. MULTI PURPOSE	64.79
TOTAL	379.07



APARTMENT AREAS				
	TYPE	APARTMENT (AREA)	BALCONY AREA	NET AREA
UNIT-1	2BR	118.48	96.45	214.93
UNIT-2	2BR	157.92	36.01	193.93
UNIT-3	2BR	189.62	33.50	223.12
UNIT-4	2BR	189.62	33.50	223.12
UNIT-5	2BR	157.92	36.01	193.93
UNIT-6	2BR	118.48	96.45	214.93
TOTAL		932.04	331.92	1263.96

FIRST FLOOR LEVEL		
RESIDENTIAL		2250.85m²
TECHNICAL		59.71m²

GENERAL NOTES :
THIS DRAWING IS THE COPYRIGHT OF LACASA Architects & Engineering
Consultant: P.O. Box 24263, DAFNA, QATAR TEL: 00974-44882939
FAX: 00974-44882767
IT IS NOT ALLOWED TO COPY OR REPRODUCE IT'S CONTENTS IN ANY FORM EXCEPT FOR THE PURPOSE WHICH IT IS INTENDED WITHOUT THE ABOVE CONSULTANT'S AUTHORITY.
DO NOT SCALE THIS DRAWING, ONLY STATED DIMENSIONS ARE TO BE CONSIDERED.
CONTRACTOR TO VERIFY THE DETAIL / INFORMATION GIVEN IN THIS DRAWING, ANY DISCREPANCIES SHALL BE BROUGHT TO ENGINEER ATTENTION PRIOR TO COMMENCEMENT OF WORK, FAILURE TO COMPLY WITH THE ABOVE WILL BE CONTRACTOR'S LIABILITY.

0.00 LVL = +3.60 QND

00	07/24/24	DETAILED DESIGN SUBMISSION	LCQ
00	01/29/24	SCHEMATIC DESIGN SUBMISSION	LCQ
Rev.	Date	Description.	By

PURPOSE OF ISSUE
DETAILED DESIGN STAGE
PROJECT TITLE
**PROPOSED 3B+G+26 FLOOR
RESIDENTIAL TWIN TOWERS
ON PLOT WR - RES/19-20
AT LUSAIL CITY, QATAR
PIN: 69051643**

CLIENT
**H.E. Dr. KHALID MOHAMED A
AL-ATTIYAH**
CONSULTANT
LACASA قطر
P.O.Box: 24263 Doha, Qatar Tel: +974 4882939 Fax: +974 4882767
Email info@lacasa.qa Website www.lacasa.qa
PROJECT NO.
PQ-22016

DRAWING TITLE
**AREA BREAKDOWN SHEET
2**

DATE ISSUE	SHT. SIZE	SCALE	DRAWN	CHECKED	APPROVED
24 JUL 24	A1	1:600	LCQ	LCQ	BAT

NORTH N	DRAWING NUMBER A-005B	REVISION 00
------------	---------------------------------	-----------------------